

Согласовано			
Взам инв. №			
Подл и дата			
Инв. № подл			

WhiteLisa

Контакты: +7 (913) 512-18-11 | Telegram: @architect_lis

Заказчик Аббасов Эльнур

городской округ Красноярск СНТ Палати ул.Зелёная д. 541

Одноэтажный жилой дом с мансардой


ул. Зелёная д. 541

26-124-EXP.BARN - 150. AP


Директор

Архитектор Лисенков Д.А.

Кладочный план на отм. 0.000 (1:100)

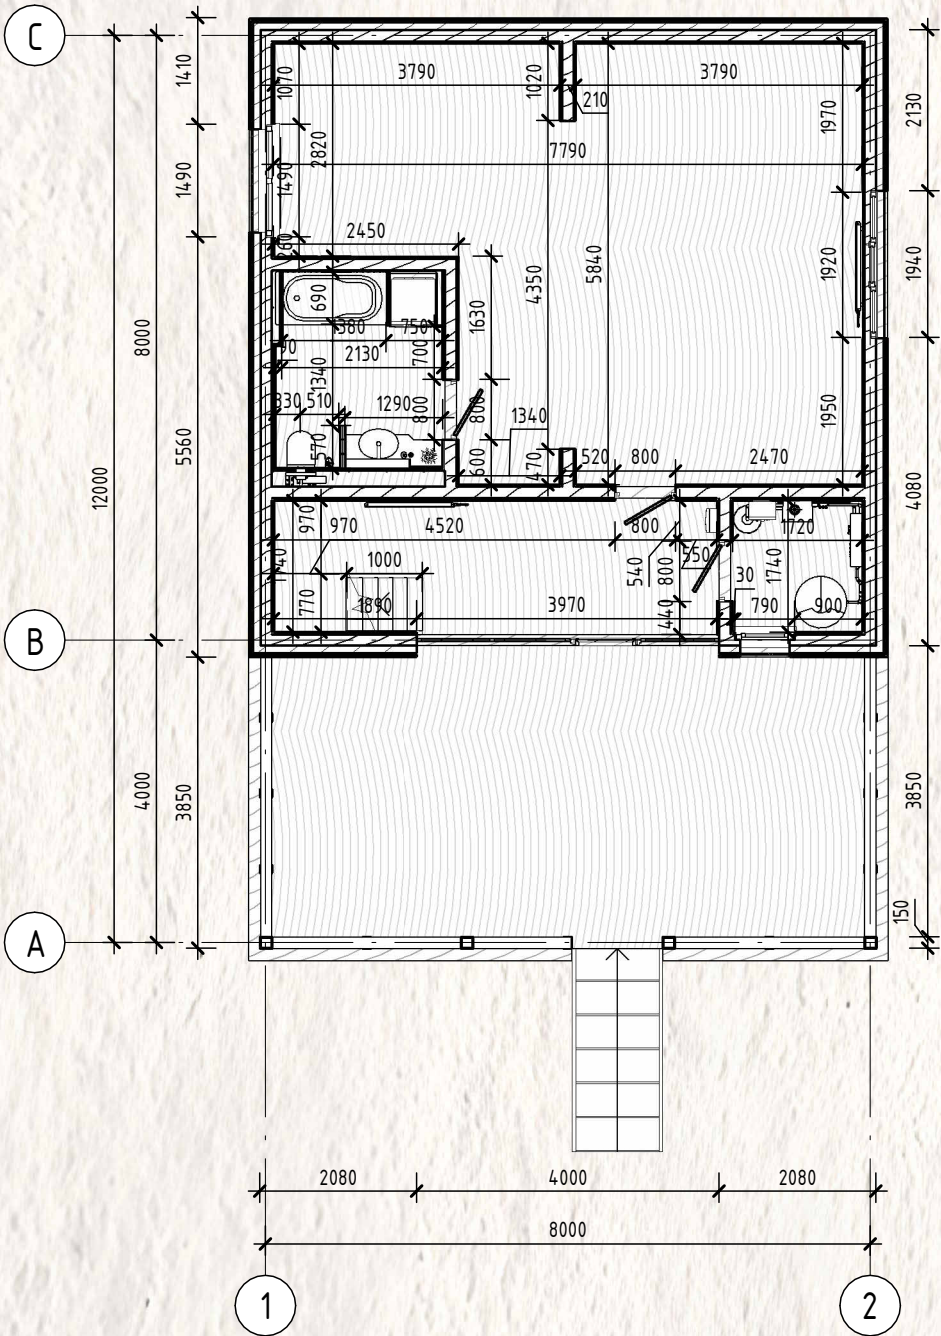

Кладочный план на отм. +3.000 М1:100

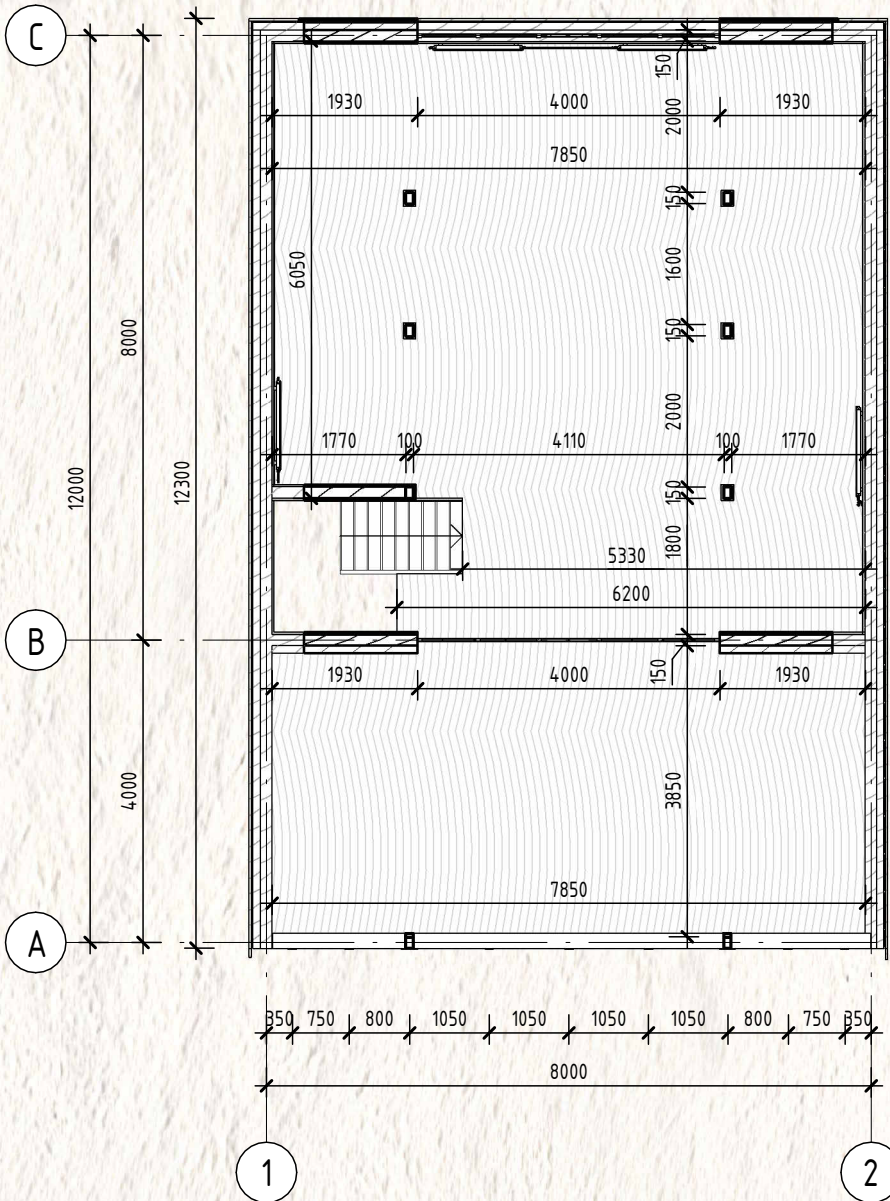

Маркировочный план 1-го этажа М1:100




Экспликация помещений

Номер помещения	Наименование	Площадь, м²	Кат. помещения
1	Комната	15,30	
2	Кухня-гостинная	22,70	
3	Санузел	6,60	
4	Тамбур	10,70	
5	Котельная	3,20	
6	Мансардный этаж	60,10	


Примечание:
1. Все размеры на плане указаны уже в чистовом виде (с учётом штукатурки +3 см на стенах).
2. При кладке самих стен (в черновом варианте) делайте отступ на толщину штукатурки, чтобы после отделки комнаты получились точно как на чертеже.
3. Перед началом работ обязательно проверьте размеры на месте.

						26-124-EXP.BARN - 150.AP			
						городской округ Красноярск СНТ Палаты ул.Зелёная д. 541			
Изм.	Кол.уч.	Лист	№ док.	Подп.	Дата	Одноэтажный жилой дом с мансардой	Стадия	Лист	Листов
Архитектор		Лисенков Д.А					РД	001	
Проверил									
Т.контр.						Кладочный план на отм. 0.000 и +3.000, Маркировочный план 1-го Этажа, Экспликация помещений	 Whitelisa		
ГАП		Лисенков Д.А							
Утвердил									

Развертка стен помещения Котельной (1:25)

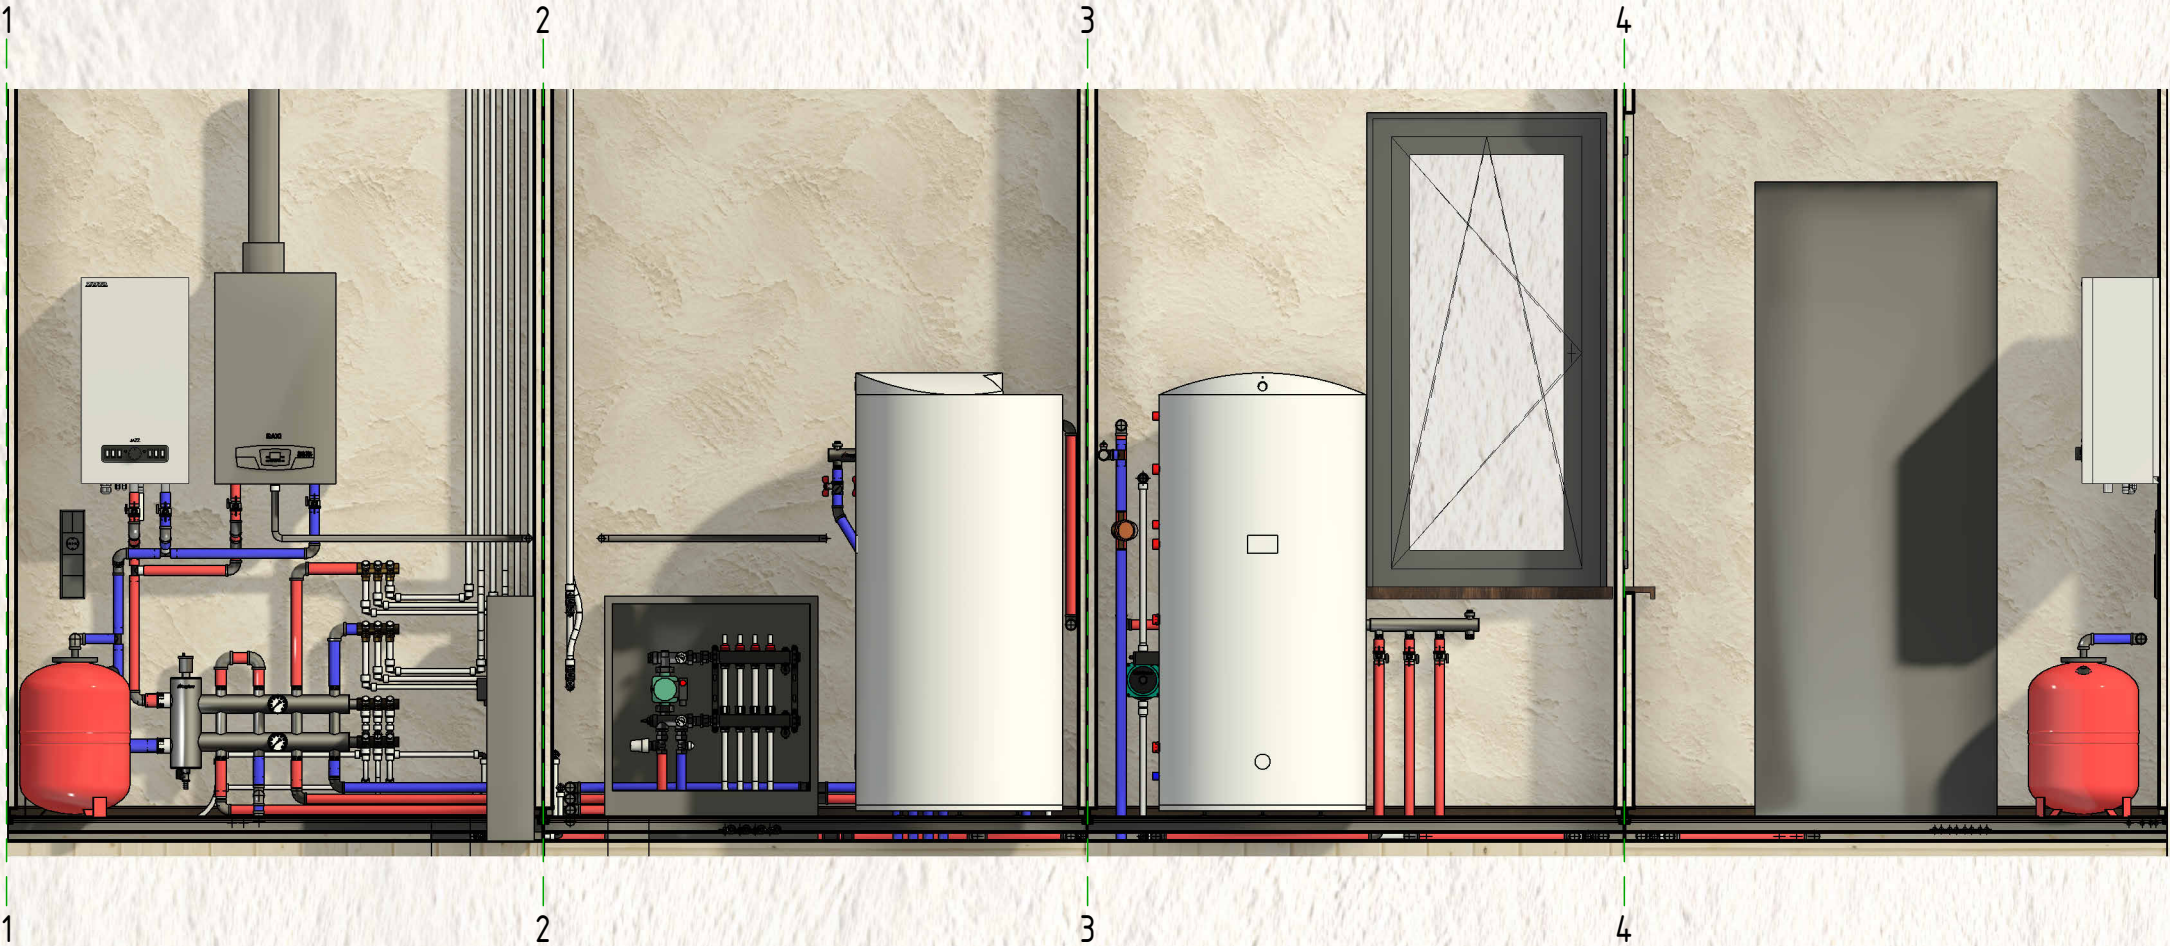

План расстановки оборудования помещения Котельной (1:25)

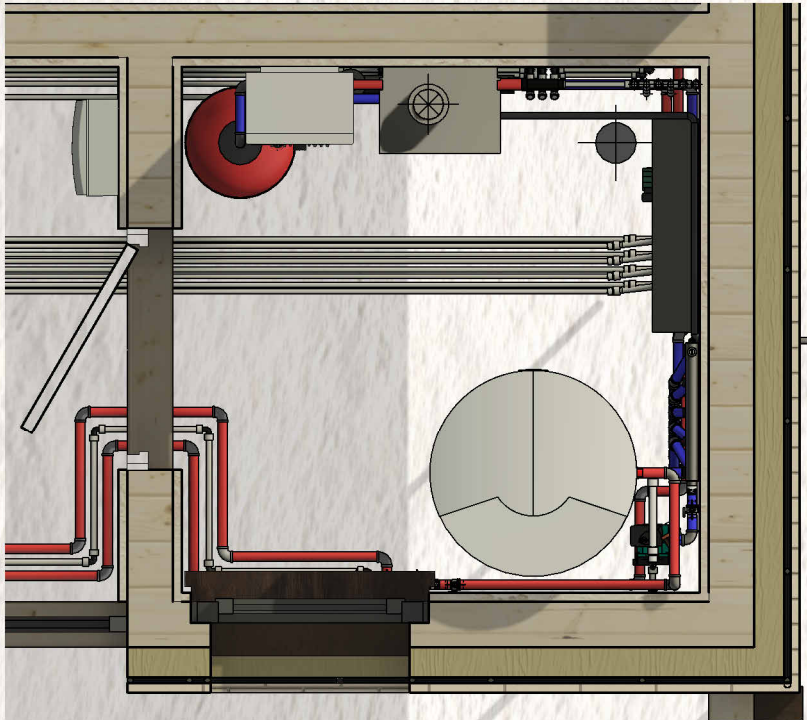

Спецификация оборудования, изделий и материалов

Поз.	Наименование и техническая характеристика	Завод-изготовитель, поставщик	Ед. изм.	Кол-во
1	USYSTEMS коллектор UN с расходомерами стальной с накидной гайкой, выходы 4 x 3/4" Евроконус	USYSTEMS	шт.	1
2	USYSTEMS насосно-смесительный блок с термостатической головкой	USYSTEMS	шт.	1
3	Бойлер косвенного нагрева напольный	ООО "Терем"	шт.	1
4	Коллектор латунный с регулирующими вентилями MVI 1"x3/4", 3 выхода	ООО Йорхе Рус	Шт.	4
5	Котел газовый настенный конденсационный Duo-Tec Compact 1.24 GA	BAXI	шт.	1
6	Котел электрический отопительный ZOTA Jazz 6 кВт	ZOTA	шт.	1
7	Малый повысительный насос PROMO 15-12A	SHINHO	шт	1
8	Расширительный бак 50л WRV50 для отопления Uni-Fitt.	Uni-Fitt	шт.	1

26-124-EXP.BARN - 150.AP

городской округа Красноярск СНТ Палаты ул.Зелёная д. 541

						26-124-EXP.BARN - 150.AP			
						городской округ Красноярск СНТ Палаты ул.Зелёная д. 541			
Изм.	Кол.уч.	Лист	№ док.	Подп.	Дата	Одноэтажный жилой дом с мансардой	Стадия	Лист	Листов
Архитектор		Лисенков Д.А.					РД	002	
Проверил									
Т.контр.						Развертка помещения Котельной	 Whitelisa		
ГАП		Лисенков Д.А.							
Утвердил									

Согласовано					
Взам. инв. №					
Подп. и дата					
Инв. № подл.					

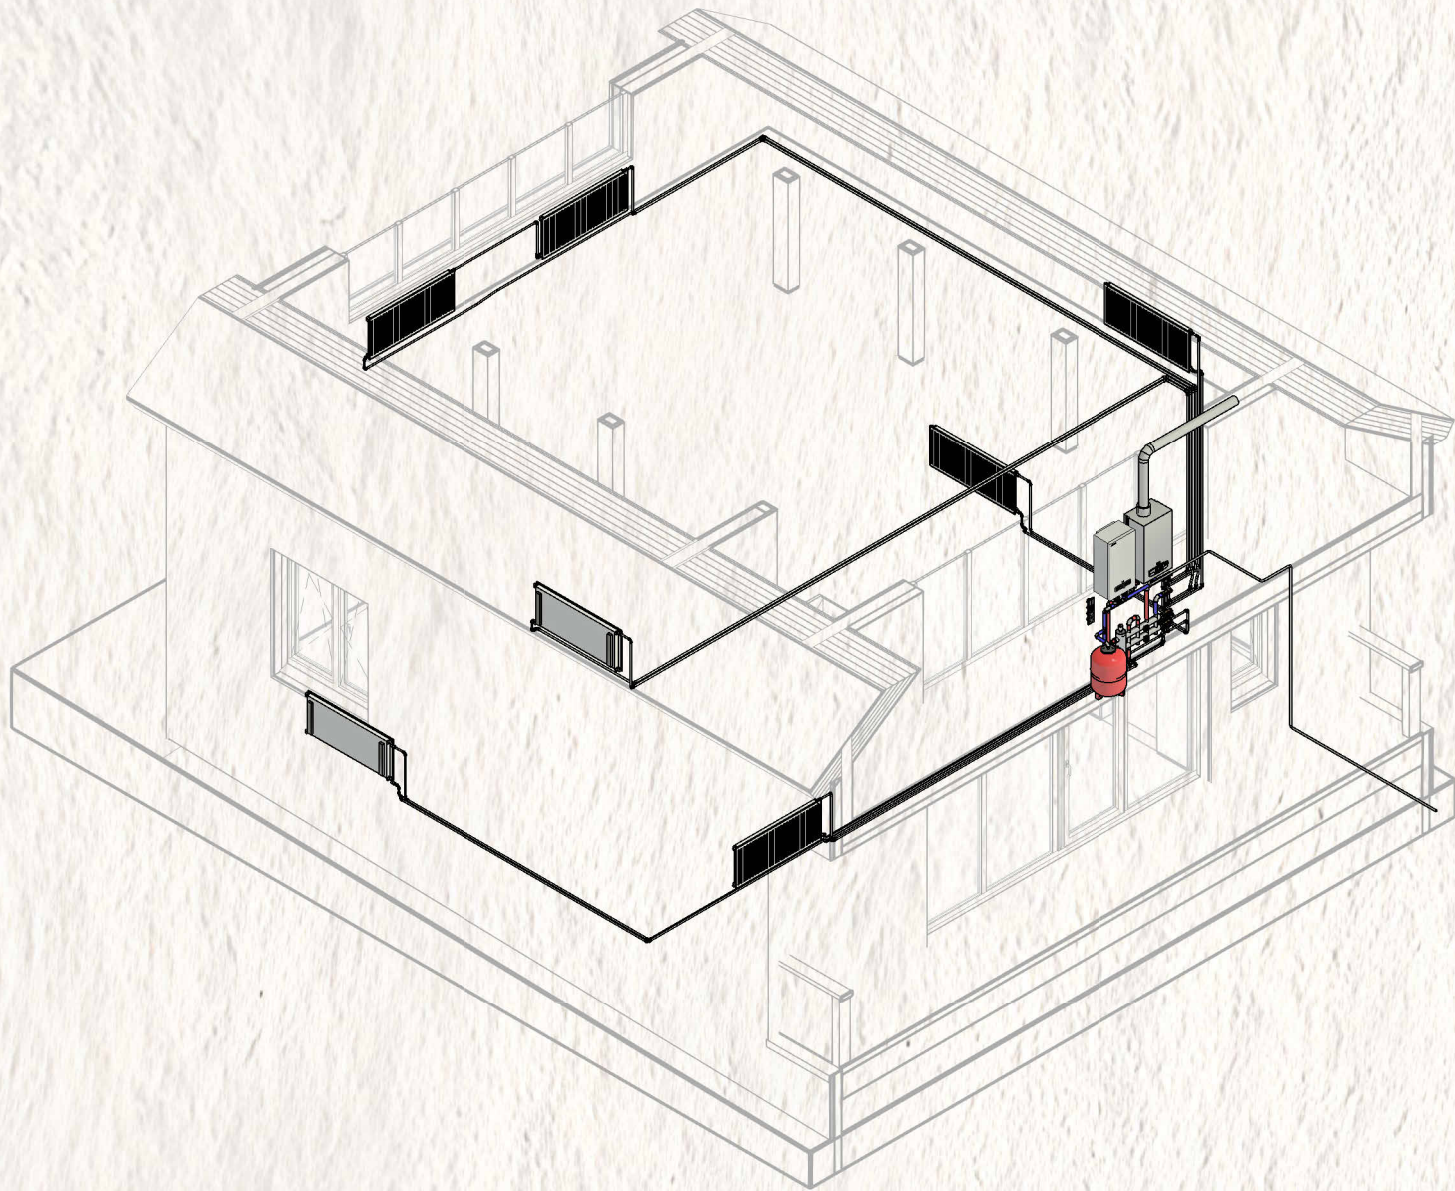


Схема системы отопления (Т1, Т2)

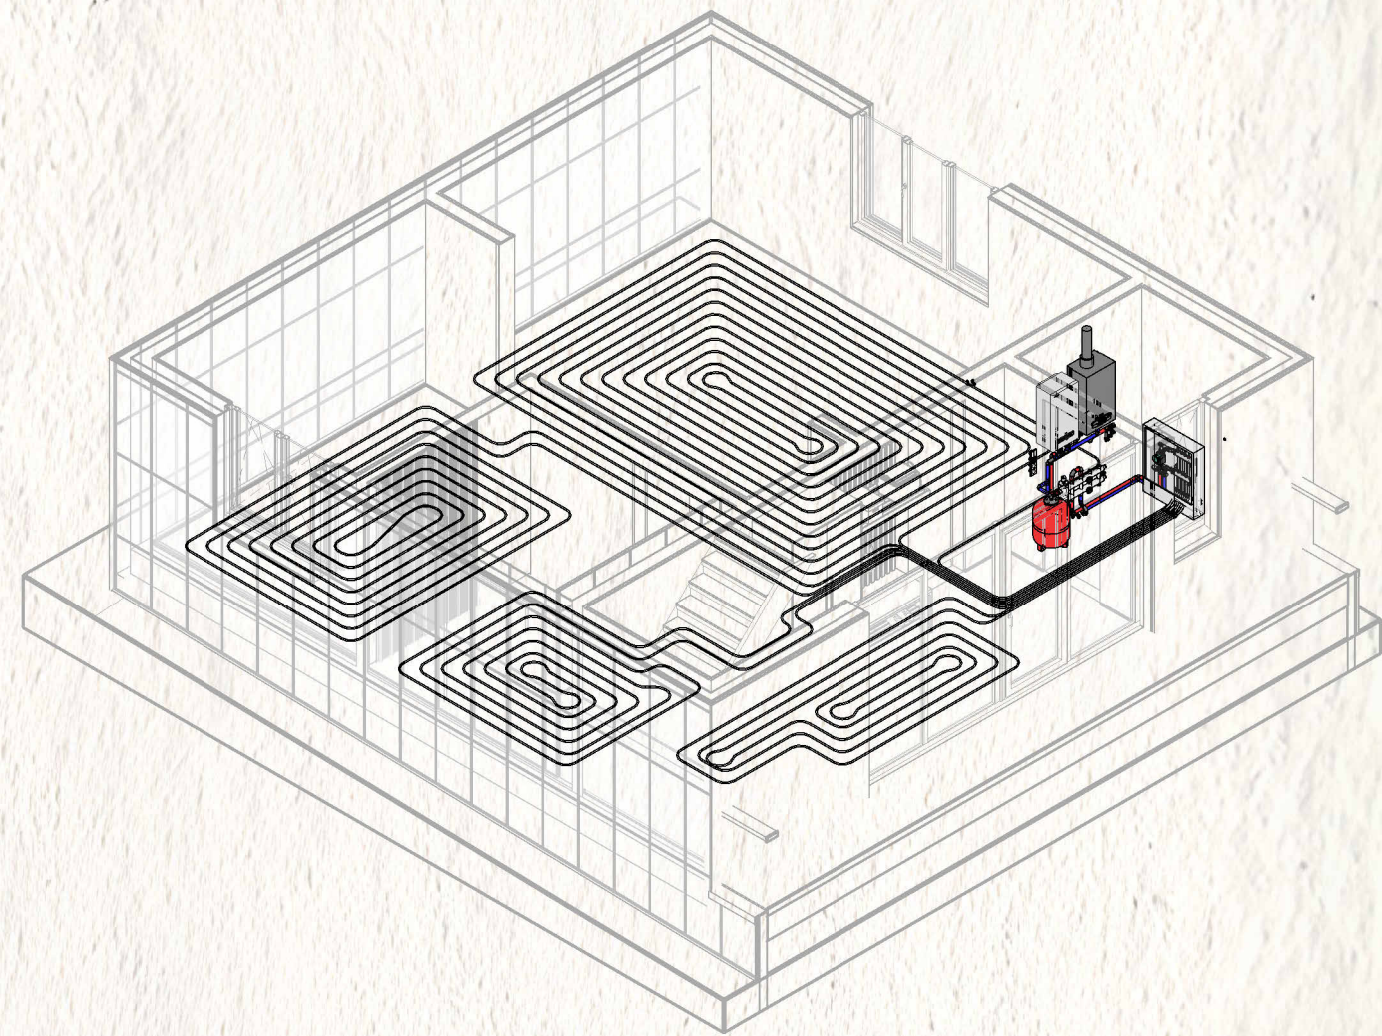
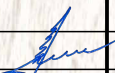


Схема системы теплых полов (Т1.1)

						26-124-EXP.BARN - 150.AP			
						городской округ Красноярск СНТ Палаты ул.Зелёная д. 541			
Изм.	Кол.уч.	Лист	№ док.	Подп.	Дата	Одноэтажный жилой дом с мансардой	Стадия	Лист	Листов
Архитектор		Лисенков Д.А.					РД	003	
Проверил									
Т.контр.						АксонOMETрические схемы систем ОВ и ВК котельной	 Whitelisa		
ГАП		Лисенков Д.А.							
Утвердил									

Согласовано		Взам. инв. №	Подп. и дата	Инв. № подл.

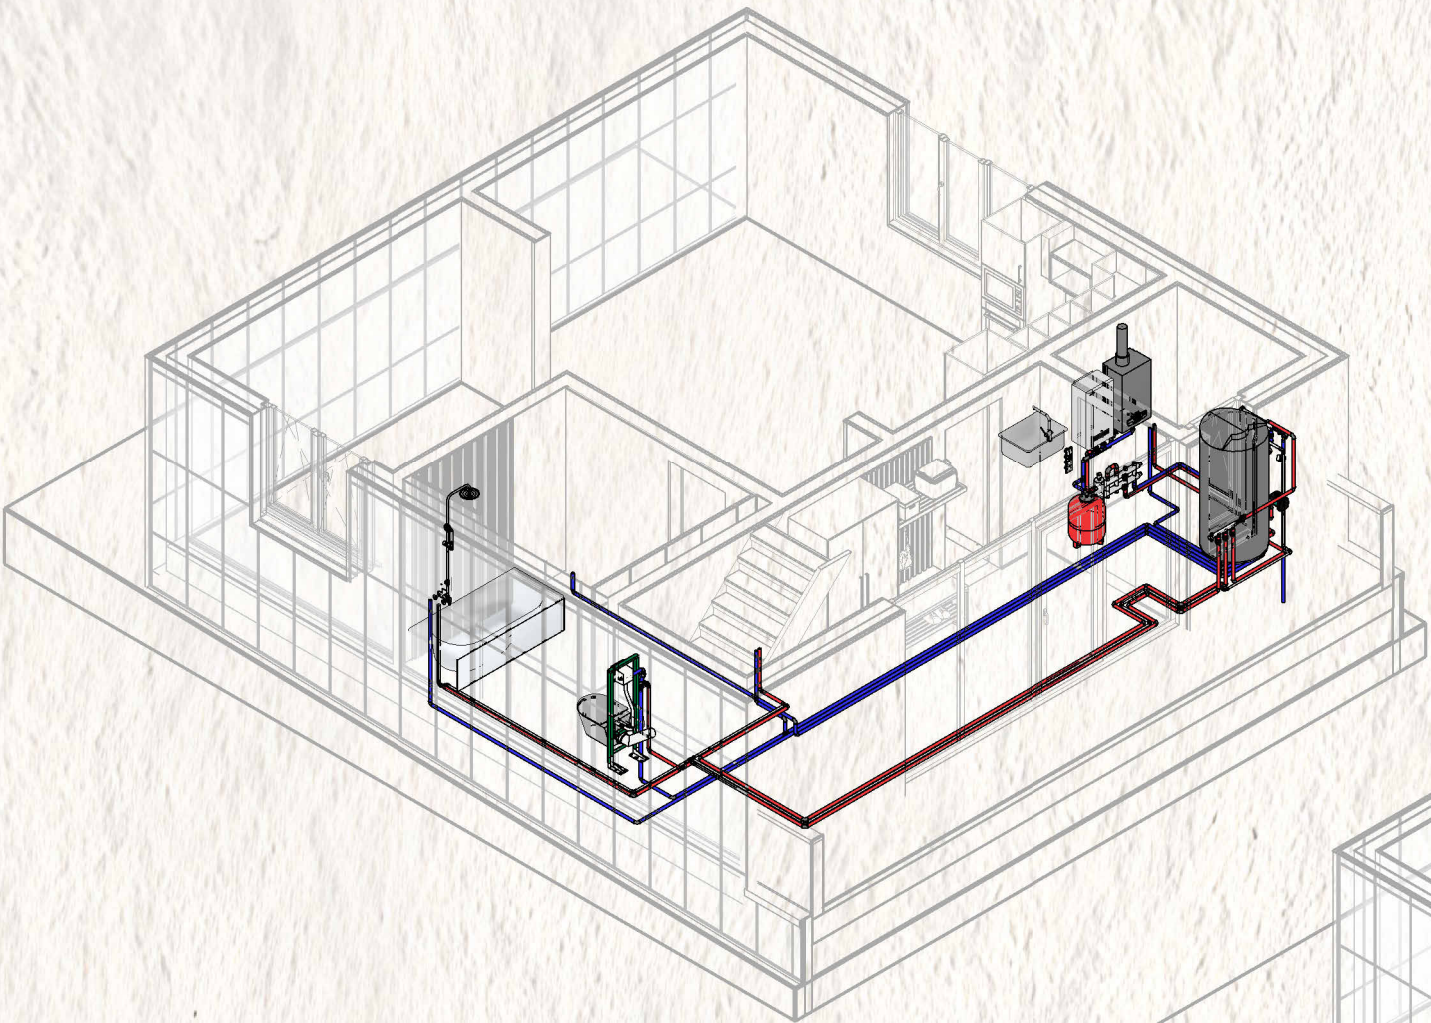


Схема систем ХВС и ГВС (В1, Т3)

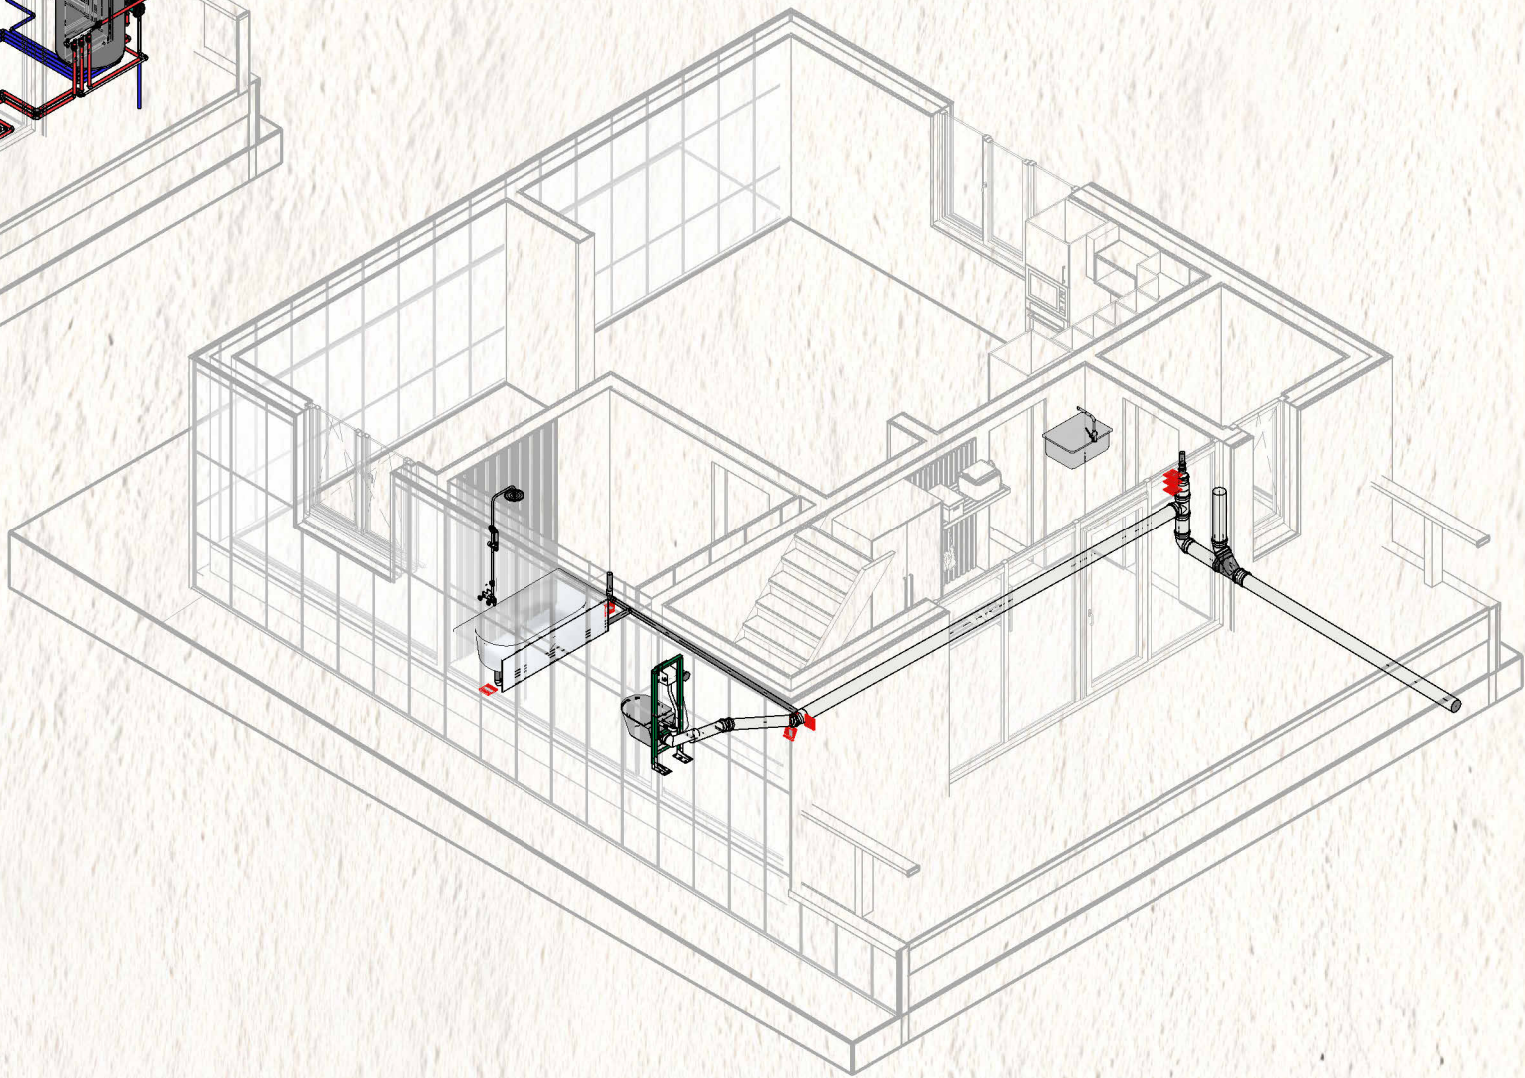


Схема системы канализации (К1)

						26-124-EXP.BARN - 150.AP			
						городской округ Красноярск СНТ Палати ул.Зелёная д. 541			
Изм.	Кол.уч.	Лист	№ док.	Подп.	Дата	Одноэтажный жилой дом с мансардой	Стадия	Лист	Листов
Архитектор		Лисенков Д.А.					РД	004	
Проверил									
Т.контр.						Аксонетрические схемы систем ОВ и ВК котельной	 Whitelisa		
ГАП		Лисенков Д.А.							
Утвердил									